


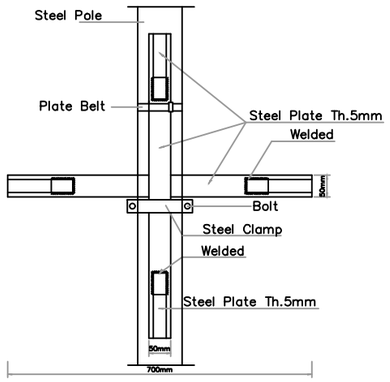



CABLE SLACK HANGER DETAIL

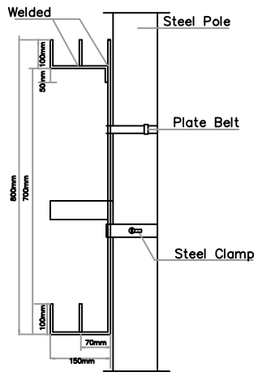


BACK SIDE

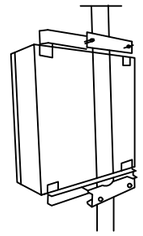

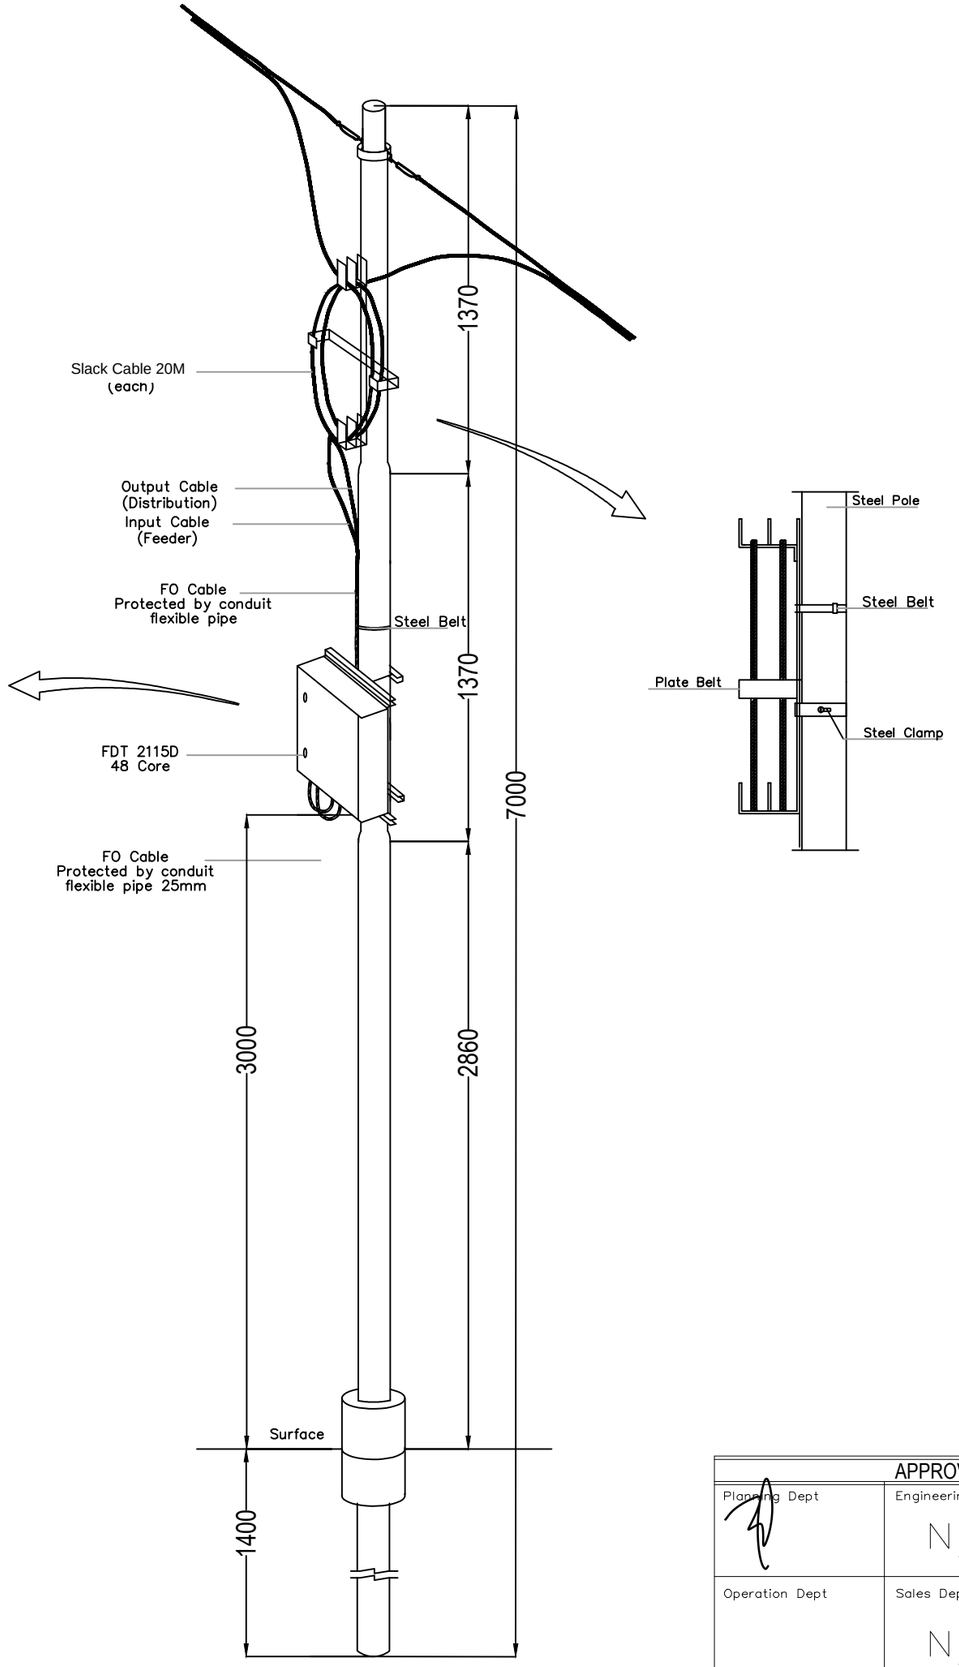



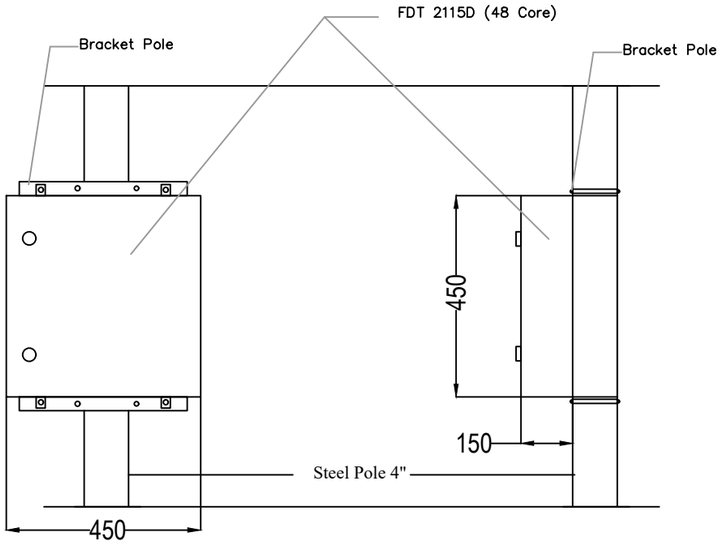


# LEGEND

| | |
|---|---|
| HUB / CENTRAL OFFICE | HANDHOLE 40X40X60 |
| SUB HUB / OPTICAL LINE TERMINAL | UNDERGROUND PEDESTAL |
| FDT FIBER DISTRIBUTION TERMINAL | NP PROPOSES NEW POLE 9m |
| FAT FIBER ACCESS TERMINAL / FAT **= SPLITTER CONFIG | NP PROPOSED NEW POLE 7m |
| OTB OPTICAL TERMINATION BOX | GARDU PLN |
| HH HANDHOLE 80X80X130 | STO TELKOM RUMAH KABEL TELKOM |
| ONT-RES (RESIDENTIAL) OPTICAL NETWORK TERMINAL | LARGE TEE RADIUS |
| ONT-MDU (BUILDING) OPTICAL NETWORK TERMINAL | CR CABLE RISER |
| FIBER OPTIC CLOSURE | BA BORING ASPAL / BORING ASPHALT WORK |
| FIGURE EIGHT / FIBER SPARE COIL | BT BORING TANAH / BORING SOIL WORK |
| Sidewalk Guy / Down Guy | GT GALI TANAH / TRENCHING TYPE WORK |

## CABLE TYPE

| | |
|---|---|
| AERIAL STRAND | FIBER 12/2T |
| UNDERGROUND STRAND | FIBER 24/4T |
| UC DROP DUCT | FIBER 36/6T |
| FEEDER CABLE ROUTE | FIBER 72/6T |
| FAT AREA LINE | FIBER 96/8T |
| | FIBER 144/12T |
| | FIBER 288/24T |

Keterangan
Note

| No. | DATE | REVISION | SIGN |
|---|---|---|---|
| | | | |
| | | | |
| | | | |

MyRepublic Plaza 1st Floor
Green Office Park 6
BSD – Tangerang 15345
Tel: +6221 319 2626

POLE MOUNTED FDT 48C INSTALATION
(POLE 7M)

Nama Proyek
Project Name

Tipe Gambar
Drawing Type
AS PLAN DESIGN FTTH NETWORK

## DRAWING SIGN & CHECK

| | |
|---|---|
| Digambar / Drawn | Tanggal / Date |
| Diperiksa / Checked | Tanggal / Date |

| | |
|---|---|
| Hub Plan Name / Nama Rencana Hub | OLT/ Sub Hub Plan Name / Nama Rencana OLT / Sub Hub |
| Koordinat FDT / Ref / Coordinated FDT / Ref | Revisi / Revision |
| Ref. Peta / Map Ref. | No. Gambar / Drawing No. |
| Arah / Direction N | Skala / Scale |
| | Halaman / Page |

## APPROVAL MATRIX

| | | |
|---|---|---|
| Planning Dept | Engineering Dept | Project Dept |
| | N/A | |
| Operation Dept | Sales Dept | Vendor/Contractor |
| | N/A | N/A |