
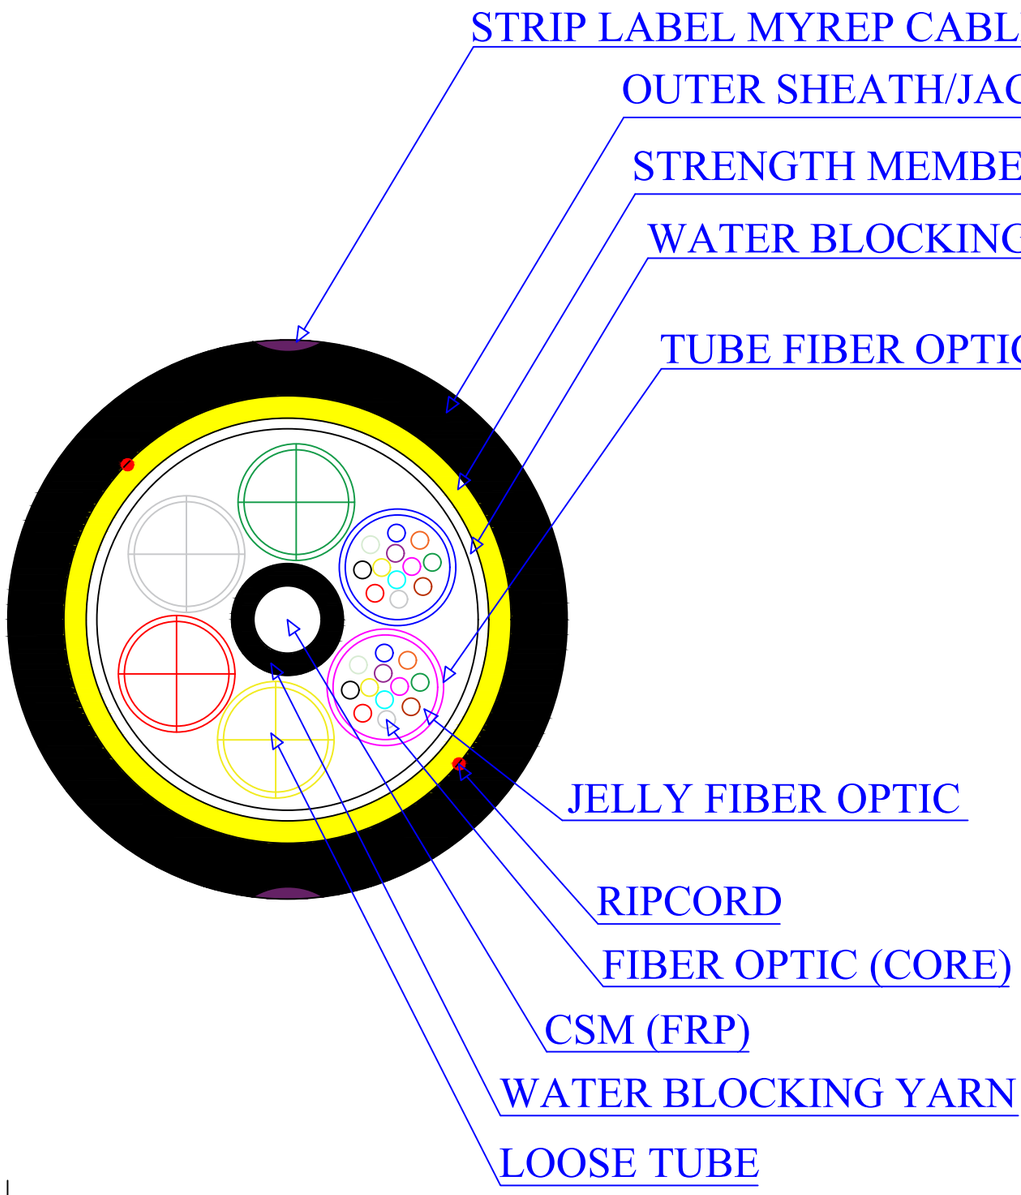


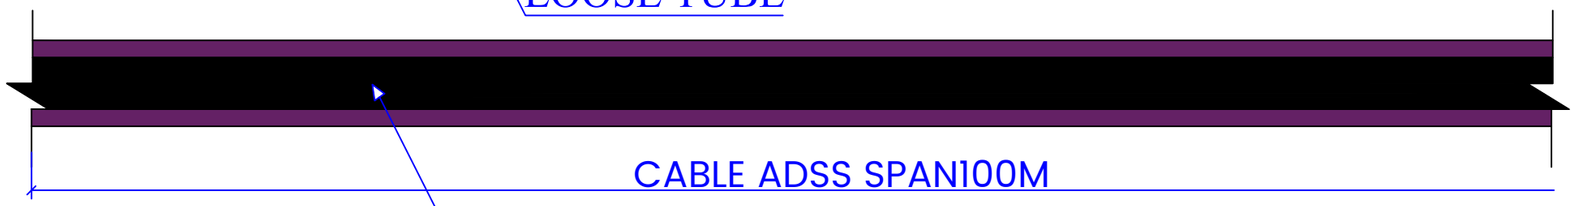

KETENTUAN CABLE MARKING

CONTOH MARKING :

MYREPUBLIC <SUPPLIER> 24/2T ITU-T G652D ADSS 2024 0000/0000 M

SPESIFIKASI TEKNIS

1	PHYSICAL : FIBER COUNT 24 CORE G652D JUMLAH FO/CORE PER TUBE 12 CORE JUMLAH TUBE 2 (FO)+4 LOOSE TUBE WARNA CORE & TUBE (ITU-T G652D) DIMENSI LUAR CABLE 10.00 ± 0.50 MM BERAT CABLE 82 KG/KM ± 15% MAKSIMUM SPAN 100 M
2	MECHANICAL : MAKSIMAL TENSILE LOAD 3200 N CRUSH RESISTANCE 2500 N/100 MM BENDING RADIUS 15*D (Ø CABLE) WIND SPEED MAX 100 KM/H, SAG 1-2% BENDING RADIUS 15*D (Ø CABLE)
3	WARNA CABLE HITAM, STRIP UNGU
4	MARKING CABLE : - FONT SIZE WIDTH 2.00 - 4.00 MM - FONT TYPE "ARIAL" - COLOR MARKING CABLE WHITE
5	FO 24 CORE UNTUK CLUSTER

APPROVAL MATRIX

PLANNING DEPT	PROJECT DEPT	OPERATION DEPT	CTO MYREPUBLIC
KRESNO AGUNG NUGROHO	PUJI YUWONO	ANGGA WISHNU WIJAYA	HENDRA GUNAWAN

LEGEND

HUB / CENTRAL OFFICE	HANDHOLE 40X40X60
SUB HUB / OPTICAL LINE TERMINAL	UNDERGROUND PEDESTAL
FDT FIBER DISTRIBUTION TERMINAL	NP PROPOSES NEW POLE 9m
FAT FIBER ACCESS TERMINAL / FAT **= SPLITTER CONFIG	NP PROPOSED NEW POLE 7m
OTB OPTICAL TERMINATION BOX	PLN GARDU PLN
HH HANDHOLE 80X80X130	STO TELKOM RUMAH KABEL TELKOM
HH HANDHOLE 20X20X20	LABEL CABLE
ONT-RES (RESIDENTIAL) OPTICAL NETWORK TERMINAL	LARGE TEE RADIUS
ONT-MDU (BUILDING) OPTICAL NETWORK TERMINAL	CR CABLE RISER
FIBER OPTIC CLOSURE	BA BORING ASPAL / BORING ASPHALT WORK
FIGURE EIGHT / FIBER SPARE COIL	BT BORING TANAH / BORING SOIL WORK
Sidewalk Guy Down Guy	GT GALI TANAH / TRENCHING TYPE WORK

CABLE TYPE

AERIAL STRAND	FIBER 12/2T
UNDERGROUND STRAND	FIBER 24/4T
UG DROP DUCT	FIBER 36/6T
FEEDER CABLE ROUTE	FIBER 72/6T
FAT AREA LINE	FIBER 96/8T
	FIBER 144/12T
	FIBER 288/24T

MyRepublic
MYREPUBLIC PLAZA 1ST FLOOR
GREEN OFFICE PARK 6
BSD – TANGERANG 15345
Tel: +6221 319 2626

NAMA PROYEK / PROJECT NAME

STANDARD DESIGN CABLE 24C SPECIFICATION

DRAWING SIGN & CHECK

DIGAMBAR / DRAWN	TANGGAL / DATE	TANDA TANGAN / SIGNATURE
WAHYU SETIYONO	18/10/2023	
DIPERIKSA / CHECKED	**TANGGAL / DATE**	**TANDA TANGAN / SIGNATURE**
SAIPULLAH HAILANI	18/10/2023	

RIWAYAT DOKUMEN / DOCUMENT HISTORY

1. REV.01 – 092021
2. REV.02 – 092022
3. REV.03 – 102023

KATEGORI GAMBAR / DESIGN CATEGORY: AERIAL & UNDERGROUND	REVISI / REVISION: REV.03
SATUAN / UNIT: SATUAN DALAM MM	SKALA / SCALE: 1 ; 100
ARAH / DIRECTION: N	NO. DOKUMEN / DOCUMENT NO: 001/AE-UG/EMR-PLG/X/2023
	NO. GAMBAR / DRAWING NO: 001