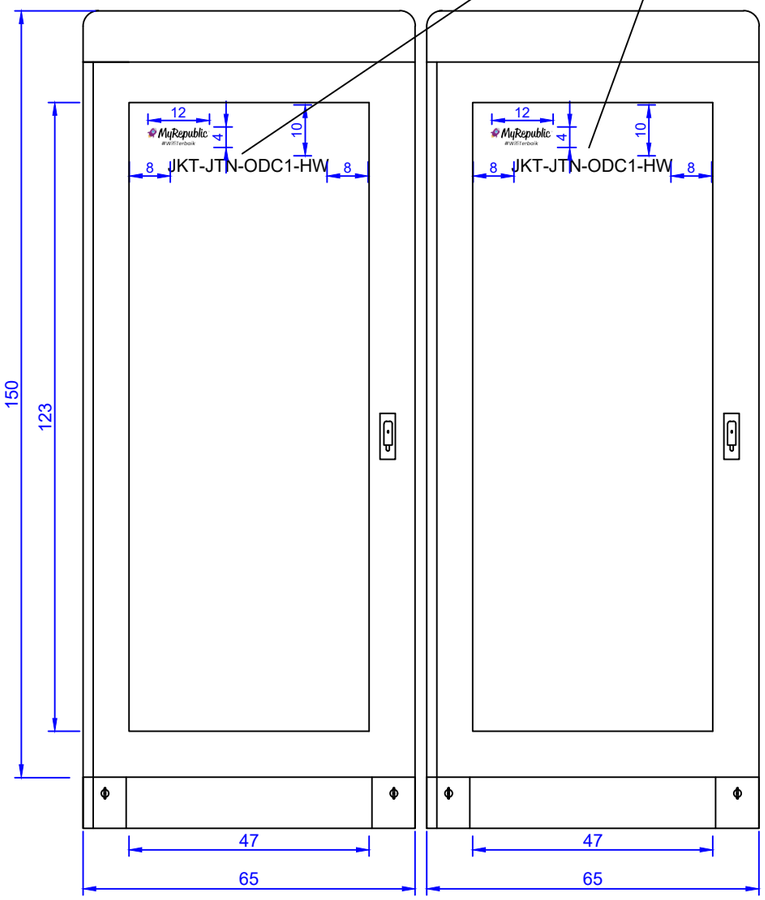


TAMPAK DEPAN

SPESIFICATION DETAIL

LABEL MATERIAL	: WATERPROOF VINYL STICKER GLOSSY WITH FINISHING METHOD
FINISHING LABEL	: PILOX CLEAR SPRAY
FONT STYLE	: POPPINS
FONT COLOR	: BLACK
FONT SIZE	: 250 pts
ODC NAME	: REFER TO HOSTNAME OLT
NOTE	: HIGH QUALITY STICKER GLASS

INFORMATION DETAIL

JKT	: JAKARTA
JTN	: JATINEGARA
ODC1	: 1st ODC
HW	: BRAND OLT HUAWEI

STICKER DIMENSION DETAIL

CODING ODC
- TOP ALIGATE : 10 cm
- LEFT RIGHT ALIGATE : 8 cm
- FONT SIZE : 250 pts

MYREPUBLIC (PROPORTIONAL ON THE TOP LEFT EDGE)
- DIMENSION : 12 cm x 4 cm

DESIGN MARKING/LABELING ODC OLT HUAWEI

LEGEND

HUB / CENTRAL OFFICE	HANDHOLE 40X40X60
SUB HUB / OPTICAL LINE TERMINAL	UNDERGROUND PEDESTAL
FDT FIBER DISTRIBUTION TERMINAL	NP PROPOSES NEW POLE 9m
FAT FIBER ACCESS TERMINAL / FAT **= SPLITTER CONFIG	NP PROPOSED NEW POLE 7m
OTB OPTICAL TERMINATION BOX	PLN GARDU PLN
HH HANDHOLE 80X80X130	STO TELKOM RUMAH KABEL TELKOM
HH HANDHOLE 20X20X20	LABEL CABLE LABEL CABLE
ONT–RES (RESIDENTIAL) OPTICAL NETWORK TERMINAL	LARGE TEE RADIUS
ONT–MDU (BUILDING) OPTICAL NETWORK TERMINAL	CR CABLE RISER
FIBER OPTIC CLOSURE	BA BORING ASPAL / BORING ASPHALT WORK
FIGURE EIGHT / FIBER SPARE COIL	BT BORING TANAH / BORING SOIL WORK
Sidewalk Guy / Down Guy	GT GALI TANAH / TRENCHING TYPE WORK

CABLE TYPE

AERIAL STRAND	FIBER 12/2T
UNDERGROUND STRAND	FIBER 24/4T
UG DROP DUCT	FIBER 36/6T
FEEDER CABLE ROUTE	FIBER 72/6T
FAT AREA LINE	FIBER 96/8T
	FIBER 144/12T
	FIBER 288/24T

MyRepublic
MYREPUBLIC PLAZA 1ST FLOOR
GREEN OFFICE PARK 6
BSD – TANGERANG 15345
Tel: +6221 319 2626

NAMA PROYEK / PROJECT NAME
STANDARD DESIGN MARKING ODC OLT HUAWEI 2024

DRAWING SIGN & CHECK

DIGAMBAR / DRAWN: WAHYU SETIYONO	TANGGAL / DATE: 04/10/2024	TANDA TANGAN / SIGNATURE
DIPERIKSA / CHECKED: SAIPULLAH HAILANI	TANGGAL / DATE: 04/10/2024	TANDA TANGAN / SIGNATURE

RIWAYAT DOKUMEN / DOCUMENT HISTORY
1. RELEASE DESIGN – 04 OCTOBER 2024

REF. PETA / MAP REF.: –	REVISI / REVISION: –
SATUAN / UNIT: SATUAN DALAM CM	SKALA / SCALE: 1 : 12
ARAH / DIRECTION: N	NO. DOKUMEN / DOCUMENT NO: 070/AE–UG/EMR–PLG/X/2024
	NO. GAMBAR / DRAWING NO: 70

APPROVAL MATRIX

PLANNING DEPT	PROJECT DEPT	OPERATION DEPT	CTO MYREPUBLIC
KRESNO AGUNG NUGROHO	PUJI YUWONO	ANGGA WISHNU WIJAYA	HENDRA GUNAWAN