


DETAIL B (CLAMP INSTALLATION : CABLE TO SLING WIRE) JARAK ANTAR CLAMP PER 2.00 METER

CLAMP : MENGGUNAKAN STEEL BAND (PLUS STOPPER STEEL BAND) ATAU CLAMP GANTUNG (CLAMP 8)

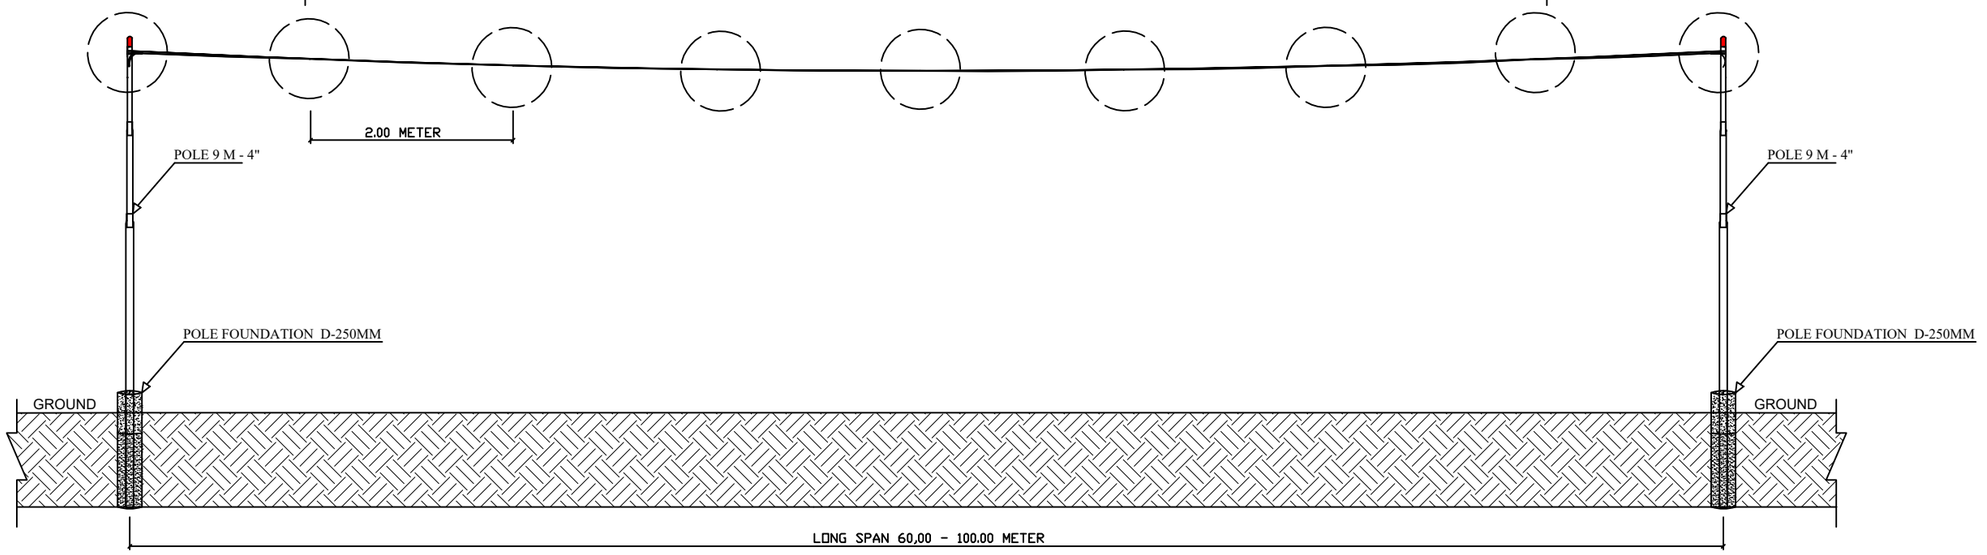

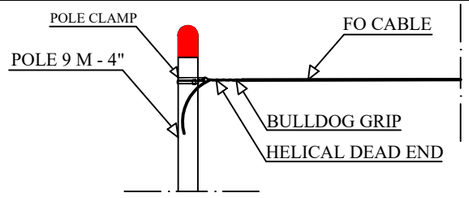

DETAIL A
(HELICAL DEAD END)

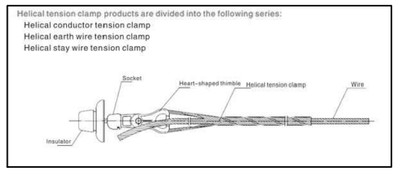


HELICAL DEAD END



POLE CLAMP



BULLDOG GRIP

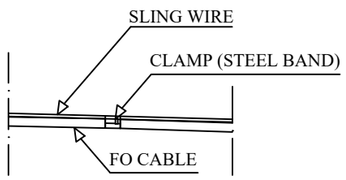


DETAIL B
(SLING WIRE WITH STEEL BAND)



SLING WIRE




STEEL BAND

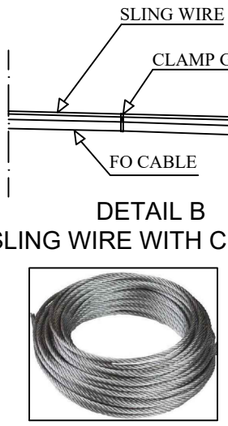

DETAIL B
(SLING WIRE WITH CLAMP 8)

SLING WIRE

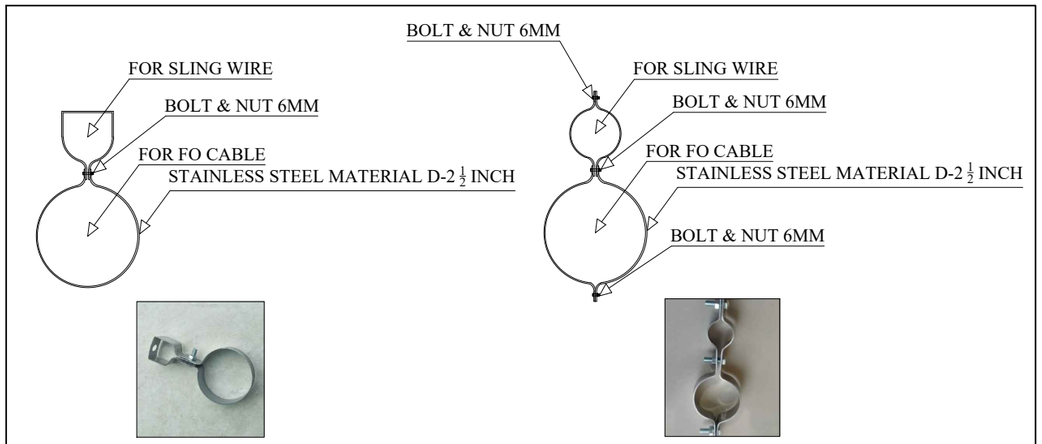

CLAMP GANTUNG (CLAMP 8) TIPE A

CLAMP GANTUNG (CLAMP 8) TIPE B

LEGEND

HUB / CENTRAL OFFICE	HANDHOLE 40X40X60
SUB HUB / OPTICAL LINE TERMINAL	UNDERGROUND PEDESTAL
FDT FIBER DISTRIBUTION TERMINAL	NP PROPOSES NEW POLE 9m
FAT FIBER ACCESS TERMINAL / FAT **= SPLITTER CONFIG	NP PROPOSED NEW POLE 7m
OTB OPTICAL TERMINATION BOX	PLN GARDU PLN
HH HANDHOLE 80X80X130	STD TELKOM RUMAH KABEL TELKOM
ONT-RES (RESIDENTIAL) OPTICAL NETWORK TERMINAL	LARGE TEE RADIUS
ONT-MDU (BUILDING) OPTICAL NETWORK TERMINAL	CR CABLE RISER
FIBER OPTIC CLOSURE	BA BORING ASPAL / BORING ASPHALT WORK
FIGURE EIGHT / FIBER SPARE COIL	BT BORING TANAH / BORING SOIL WORK
Sidewalk Guy / Down Guy	GT GALI TANAH / TRENCHING TYPE WORK

CABLE TYPE

AERIAL STRAND	FIBER 12/2T
UNDERGROUND STRAND	FIBER 24/4T
UG DROP DUCT	FIBER 36/6T
FEEDER CABLE ROUTE	FIBER 72/6T
FAT AREA LINE	FIBER 96/8T
	FIBER 144/12T
	FIBER 288/24T

MyRepublic
MYREPUBLIC PLAZA 1ST FLOOR
GREEN OFFICE PARK 6
BSD – TANGERANG 15345
Tel: +6221 319 2626

NAMA PROYEK / PROJECT NAME

STANDARD DESIGN HELICAL DEAD END < SPAN 60–100 M >
HELICAL DEAD END WITH SLING WIRE INSTALLATION

TIPE GAMBAR / DRAWING TYPE

STANDARD DESIGN FTTH NETWORK MYREPUBLIC

SPESIFIKASI TEKNIS

INSTALASI LONG SPAN 60 - 100 M :

- UNTUK FEEDER/CROSSING JALAN RAYA MENGGUNAKAN AKSESORIS HELICAL DEAD END
- POLE/TIANG YANG DIGUNAKAN YAITU POLE/TIANG 9 M - 4 INCH
- CABLE DIINSTALL DENGAN SUPPORT OLEH SLING WIRE DAN DIKAITKAN DENGAN :
  1. STEEL BAND, ATAU
  2. CLAMP GANTUNG (CLAMP 8)
- PENGAIT ANTARA CABLE & SLING WIRE DIPASANG PER 2 M

DRAWING SIGN & CHECK

DIGAMBAR / DRAWN: WAHYU SETIYONO	TANGGAL / DATE
DIPERIKSA / CHECKED	TANGGAL / DATE
NAMA RENCANA HUB / HUB PLAN NAME	NAMA RENCANA OLT/SUB HUB / OLT / SUB HUB PLAN NAME
KOORDINAT FDT/REF / FDT/REF COORDINATED	REVISI / REVISION
REF. PETA / MAP REF.	SATUAN / UNIT: SATUAN DALAM MM
ARAH / DIRECTION: N	SKALA / SCALE
	NO. GAMBAR / DRAWING NO

APPROVAL MATRIX

PLANNING DEPT	PLANNING DEPT
OPERATION DEPT	PROJEECT DEPT