




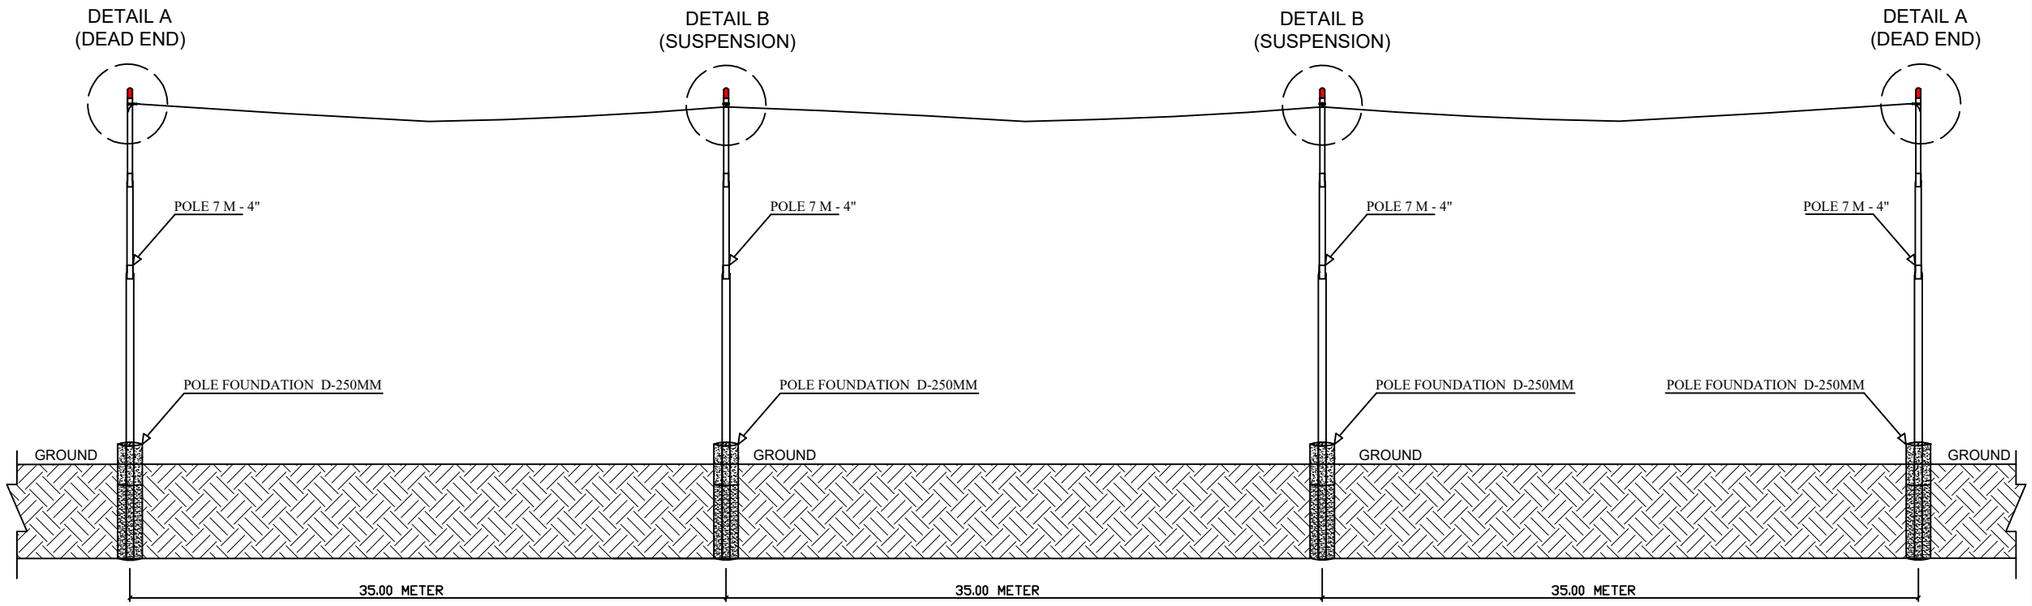

DETAIL A
(DEAD END)

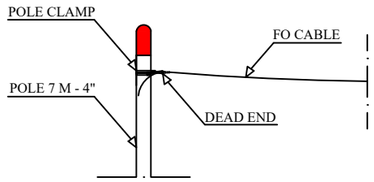

DETAIL B
(SUSPENSION)

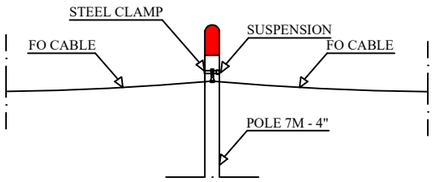

DEAD END



POLE CLAMP



SUSPENSION



STEEL CLAMP

LEGEND

HUB / CENTRAL OFFICE	HANDHOLE 40X40X60
SUB HUB / OPTICAL LINE TERMINAL	UNDERGROUND PEDESTAL
FIBER DISTRIBUTION TERMINAL	PROPOSES NEW POLE 9m
FIBER ACCESS TERMINAL / FAT **= SPLITTER CONFIG	PROPOSED NEW POLE 7m
OPTICAL TERMINATION BOX	GARDU PLN
HANDHOLE 80X80X130	RUMAH KABEL TELKOM
ONT-RES (RESIDENTIAL) OPTICAL NETWORK TERMINAL	LARGE TEE RADIUS
ONT-MDU (BUILDING) OPTICAL NETWORK TERMINAL	CABLE RISER
FIBER OPTIC CLOSURE	BORING ASPAL / BORING ASPHALT WORK
FIGURE EIGHT / FIBER SPARE COIL	BORING TANAH / BORING SOIL WORK
Sidewalk Guy / Down Guy	GALI TANAH / TRENCHING TYPE WORK

CABLE TYPE

AERIAL STRAND	FIBER 12/2T
UNDERGROUND STRAND	FIBER 24/4T
UG DROP DUCT	FIBER 36/6T
FEEDER CABLE ROUTE	FIBER 72/6T
FAT AREA LINE	FIBER 96/8T
	FIBER 144/12T
	FIBER 288/24T

MyRepublic
MYREPUBLIC PLAZA 1ST FLOOR
GREEN OFFICE PARK 6
BSD – TANGERANG 15345
Tel: +6221 319 2626

NAMA PROYEK
PROJECT NAME

STANDARD DESIGN DEAD END <SPAN 35 M> SUSPENSION <SPAN 35 M> SUSPENSION <SPAN 35 M> DEAD END

TIPE GAMBAR
DRAWING TYPE

STANDARD DESIGN FTTH NETWORK MYREPUBLIC

DRAWING SIGN & CHECK

DIGAMBAR / DRAWN: WAHYU SETIYONO	TANGGAL / DATE
DIPERIKSA / CHECKED	TANGGAL / DATE
NAMA RENCANA HUB / HUB PLAN NAME	NAMA RENCANA OLT/SUB HUB / OLT / SUB HUB PLAN NAME
KOORDINAT FDT/REF / FDT/REF COORDINATED	REVISI / REVISION
REF. PETA / MAP REF.	SATUAN / UNIT: SATUAN DALAM MM
ARAH / DIRECTION: N	SKALA / SCALE
	NO. GAMBAR / DRAWING NO

APPROVAL MATRIX

PLANNING DEPT	PLANNING DEPT
OPERATION DEPT	PROJEECT DEPT