



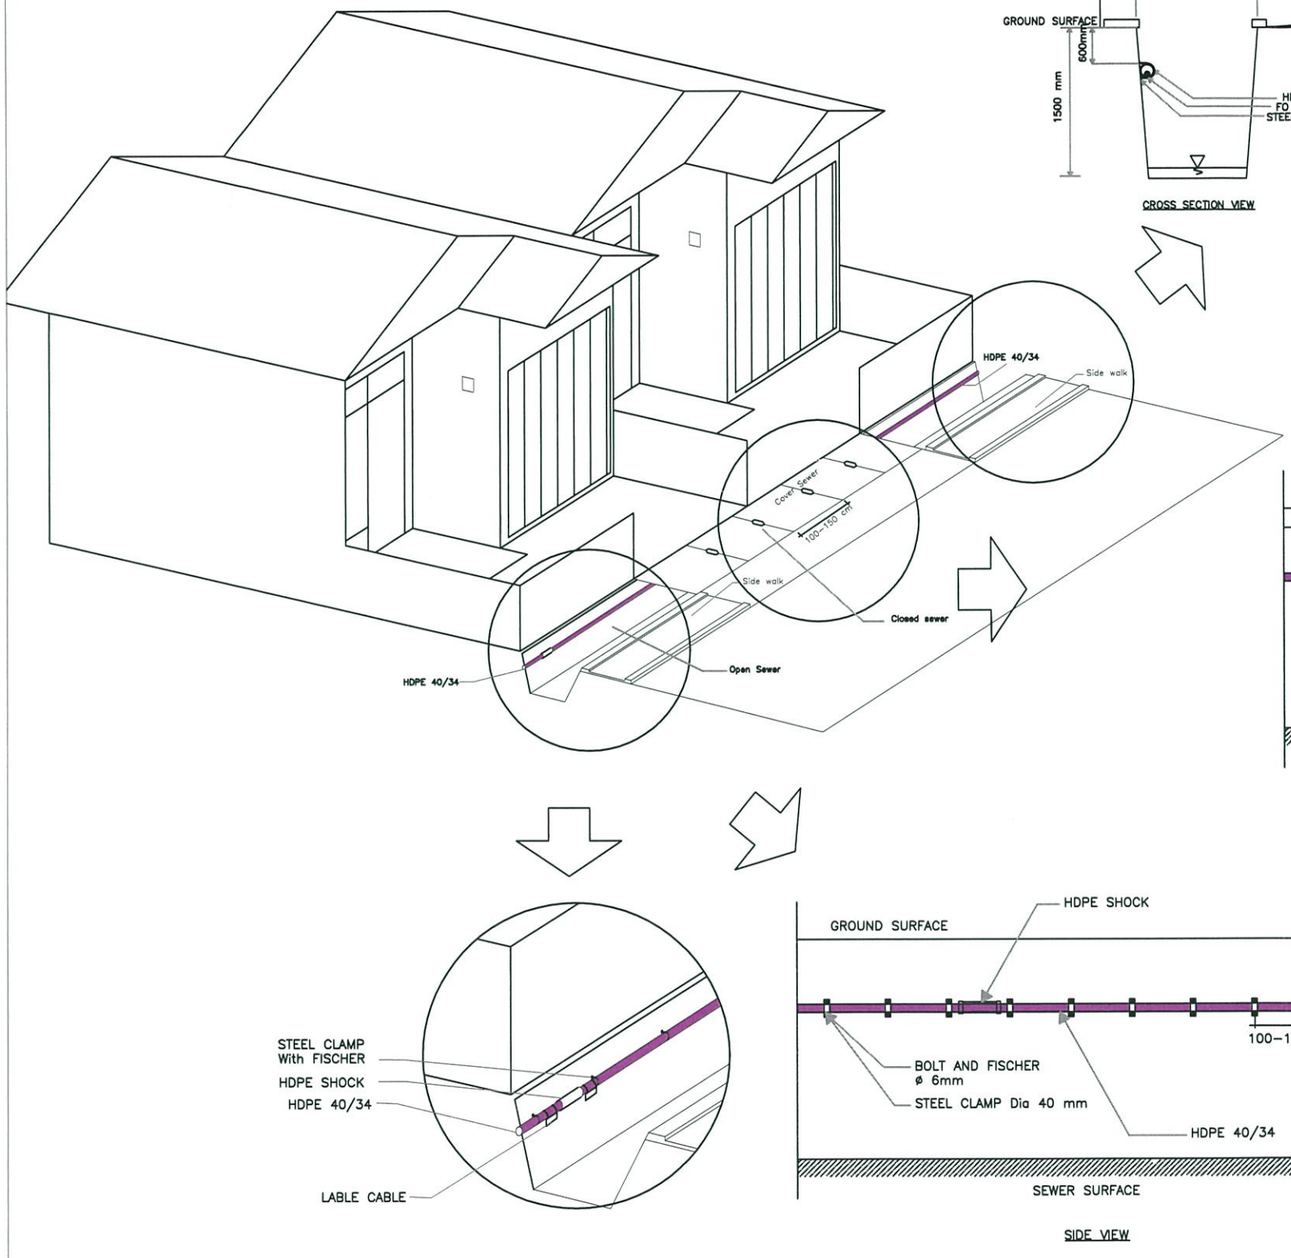


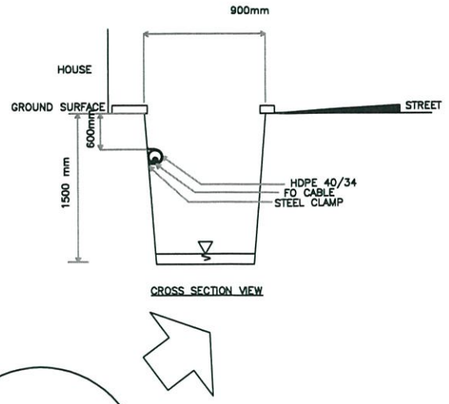

CROSS SECTION VIEW






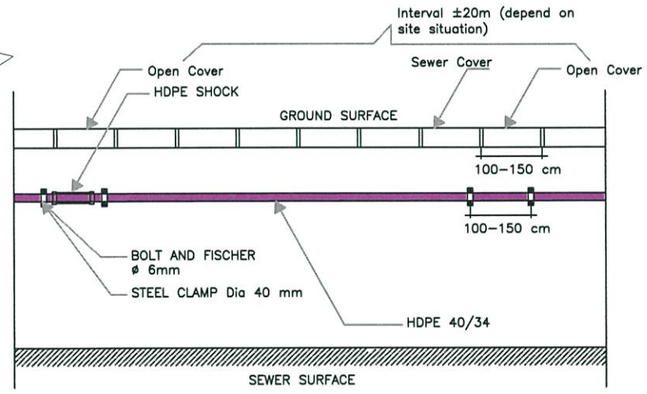
## CLOSED Sewer




SIDE VIEW

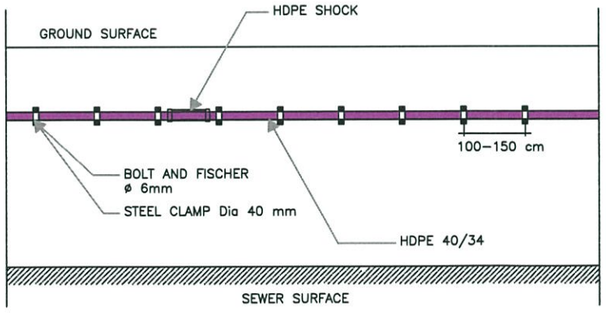


SIDE VIEW





## OPEN Sewer

DISCLAIMER :
1. THIS SOLUTION IS FOR CLUSTER WHICH NO HAVE AVAILABLE SPACE AND USE SEWER PART
2. THIS SEWER SOLUTION CAN APPLICABLE WITH CONDITION OPEN SEWER OR CLOSED SEWER WITH CAP CAN OPEN WITH SPACE AVAILABLE
3. CLOSED SEWER CANNOT HAVE ANY HDPE JOINT
4. THIS SOLUTION IS COME FROM MQM AND HUAWEI ONLY DESIGN THE SOLUTION, IF COMMUNITY REFUSE THIS SOLUTION THEN THE CLUSTER OR FEEDER WILL RETURN TO MQM

| APPROVAL MATRIX | | |
|---|---|---|
| Planning Dept. Rio 2/3-18 | Engineering Dept. | Project Dept. |
| Operation Dept. | | Vendor/Contractor |

| | |
|---|---|
| SUB HUB / OPTICAL LINE TERMINAL | UNDERGROUND PEDESTAL |
| FDT FIBER DISTRIBUTION TERMINAL | EXISTING PLN POLE |
| FAT FIBER ACCESS TERMINAL | NP PROPOSED NEW POLE |
| OTB OPTICAL TERMINATION BOX | GARDU PLN |
| PON SPLITTER WITH x SPLIT RATIO | STO RUMAH KABEL TELKOM |
| ONT-RES (RESIDENTIAL) OPTICAL NETWORK TERMINAL | CR CABLE RISER |
| ONT-MDU (BUILDING) OPTICAL NETWORK TERMINAL | BA BORING ASPAL |
| FIBER OPTIC CLOSURE | GA GALI ASPAL |
| FIGURE EIGHT / FIBER SPARE COIL | GT GALI TANAH |
| MH MANHOLE | GR GALI RUMPUT |

| | |
|---|---|
| DROPWIRE 2 CORE | FIBER 12/1T |
| AERIAL STRAND | FIBER 24/2T |
| UNDERGROUND STRAND | FIBER 48/4T |
| UG DROP DUCT | FIBER 72/6T |
| FEEDER CABLE ROUTE | FIBER 96/8T |
| | FIBER 144/12T |
| | FIBER 288/24T |

Keterangan
Note

| No. | DATE | REVISION | SIGN |
|---|---|---|---|
| | | | |
| | | | |
| | | | |
| | | | |

My Republic
My Republic Plaza 1st floor
BSD Green Office Park 6, Jalan Grand Boulevard
Tangerang Selatan 15345

PT. HUAWEI TECH INVESTMENT
BRI II Building, 17th–22nd Floor
JL. Jend. Sudirman Kav.44–46
Jakarta Pusat 10210 – Indonesia
Tel:+6221 2555 2888 – Fax:+6221 571 3178

Nama Proyek
Project Name

Tipe Gambar
Drawing Type
TYPICAL DESIGN PACK

Sewer Installation on feeder

Digambar
Drawn
Tanggal
Date

Diperiksa
Checked
Tanggal
Date

| Hub Plan Name / Nama Rencana Hub | OLT/ Sub Hub Plan Name / Nama Rencana OLT / Sub Hub |
|---|---|
| Kordinat FDT / Ref / Coordinated FDT / Ref | Revisi / Revision |
| Ref. Peta / Map Ref. | No. Gambar / Drawing No. |
| Arah / Direction N | Skala / Scale N.T.S |
| | Halaman / Page 01 OF 01 |