


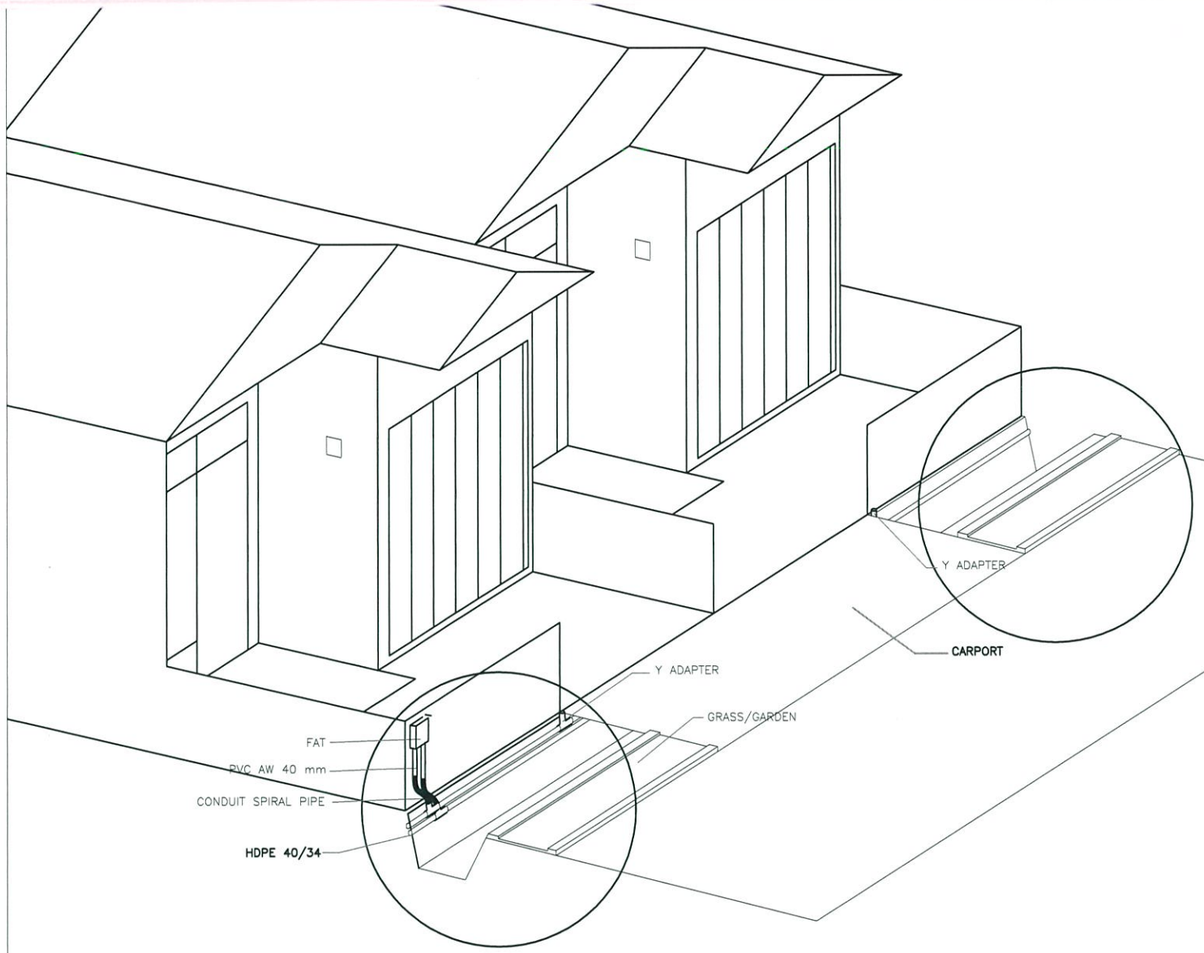


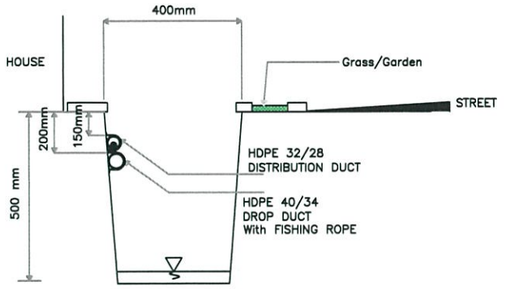


CROSS SECTION VIEW

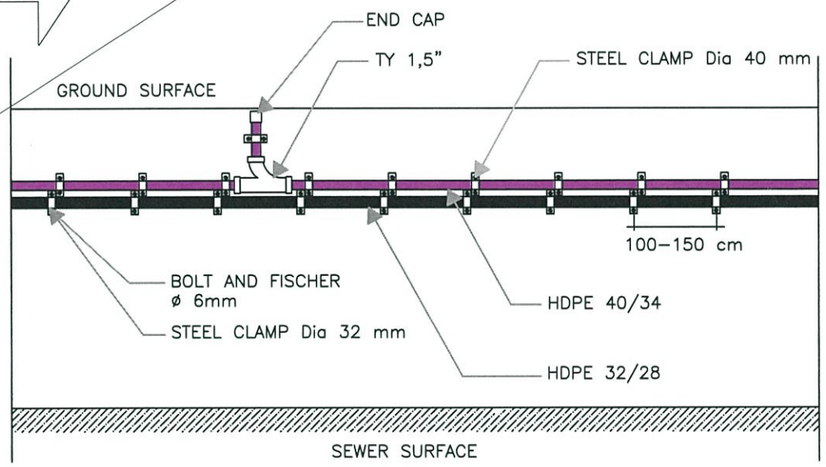

SIDE VIEW

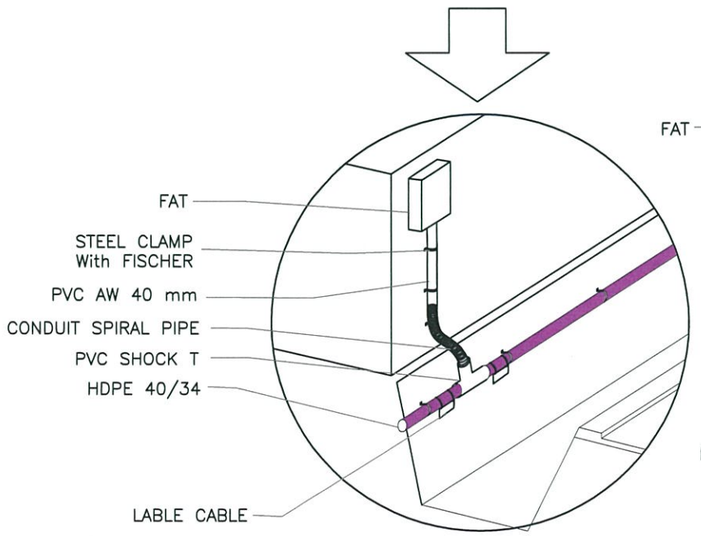

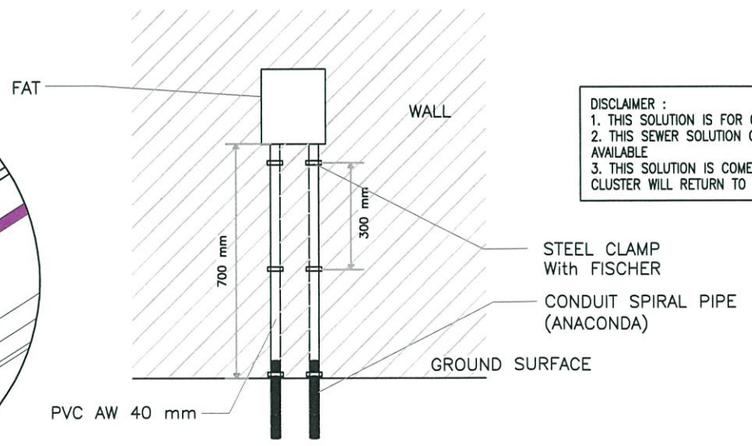

FRONT VIEW

DISCLAIMER :
1. THIS SOLUTION IS FOR CLUSTER WHICH NO HAVE AVAILABLE SPACE AND USE SEWER PART
2. THIS SEWER SOLUTION CAN APPLICABLE WITH CONDITION OPEN SEWER OR CLOSED SEWER WITH CAP CAN OPEN WITH SPACE AVAILABLE
3. THIS SOLUTION IS COME FROM MQM AND HUAWEI ONLY DESIGN THE SOLUTION, IF COMMUNITY REFUSE THIS SOLUTION THEN THE CLUSTER WILL RETURN TO MQM

APPROVAL MATRIX		
Planning Dept. Rio 3/3-18	Engineering Dept.	Project Dept.
Operation Dept.		Vendor/Contractor

HUB / CENTRAL OFFICE	HANDHOLE
SUB HUB / OPTICAL LINE TERMINAL	UNDERGROUND PEDESTAL
FDT FIBER DISTRIBUTION TERMINAL	EXISTING PLN POLE
FAT FIBER ACCESS TERMINAL	PROPOSED NEW POLE
OTB OPTICAL TERMINATION BOX	GARDU PLN
PON SPLITTER WITH x SPLIT RATIO	RUMAH KABEL TELKOM
ONT-RES (RESIDENTIAL) OPTICAL NETWORK TERMINAL	CABLE RISER
ONT-MDU (BUILDING) OPTICAL NETWORK TERMINAL	BORING ASPAL
FIBER OPTIC CLOSURE	GALI ASPAL
FIGURE EIGHT / FIBER SPARE COIL	GALI TANAH
MH MANHOLE	GALI RUMPUT

DROPWIRE 2 CORE	FIBER 12/1T
AERIAL STRAND	FIBER 24/2T
UNDERGROUND STRAND	FIBER 48/4T
UG DROP DUCT	FIBER 72/6T
FEEDER CABLE ROUTE	FIBER 96/8T
	FIBER 144/12T
	FIBER 288/24T

Keterangan
Note

No.	DATE	REVISION	SIGN

My Republic
My Republic Plaza 1st floor
BSD Green Office Park 6, Jalan Grand Boulevard
Tangerang Selatan 15345

PT. HUAWEI TECH INVESTMENT
BRI II Building, 17th–22nd Floor
Jl. Jend. Sudirman Kav.44–46
Jakarta Pusat 10210 – Indonesia
Tel: +6221 2555 2888 – Fax: +6221 571 3178

Nama Proyek / Project Name

Tipe Gambar / Drawing Type
TYPICAL DESIGN PACK

Sewer Installation on wall

Digambar / Drawn | Tanggal / Date

Diperiksa / Checked | Tanggal / Date

Hub Plan Name / Nama Rencana Hub | OLT/ Sub Hub Plan Name / Nama Rencana OLT / Sub Hub

Koordinat FDT / Ref / Coordinated FDT / Ref | Revisi / Revision

Ref. Peta / Map Ref. | No. Gambar / Drawing No.

Arah / Direction: N | Skala / Scale: N.T.S

Halaman / Page: 01 OF 01