


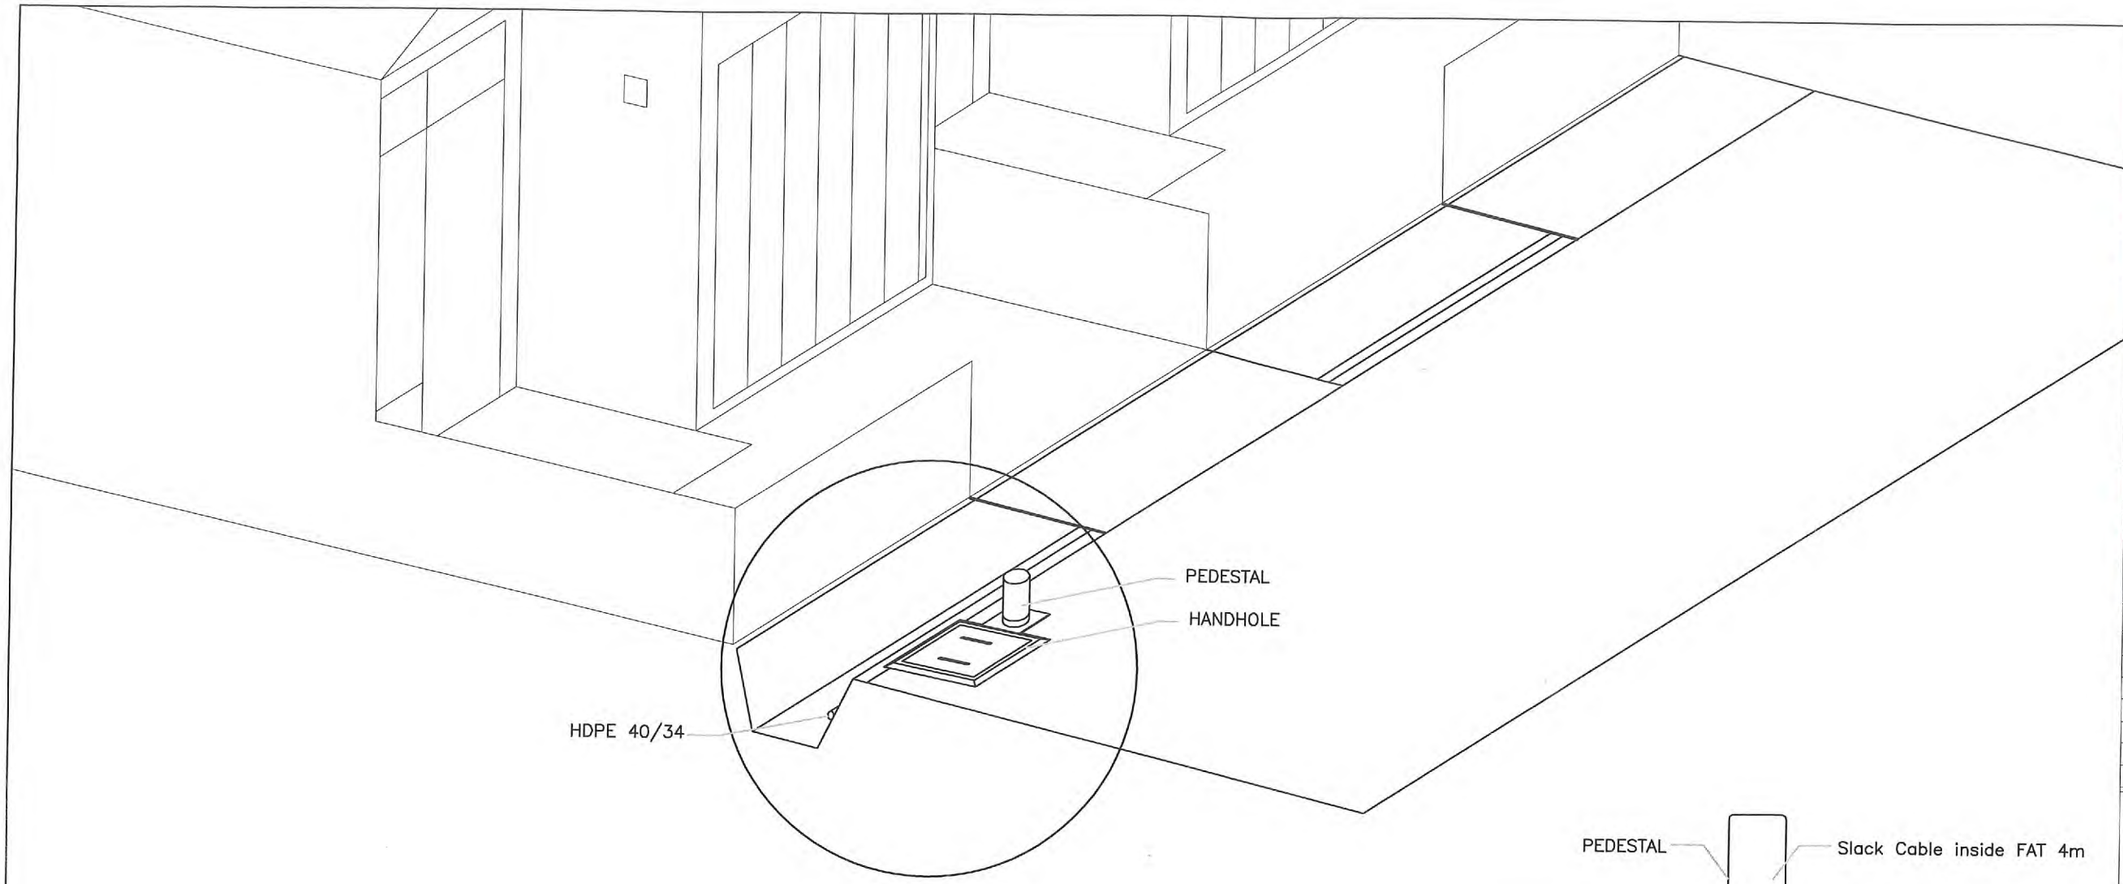


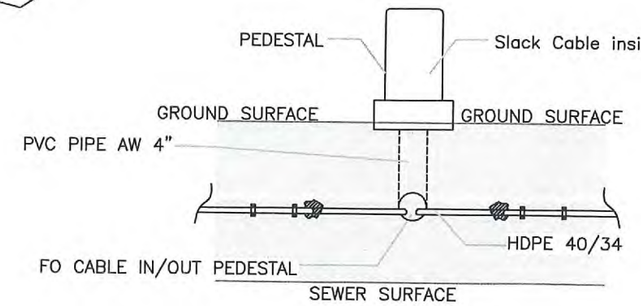

CROSS SECTION VIEW

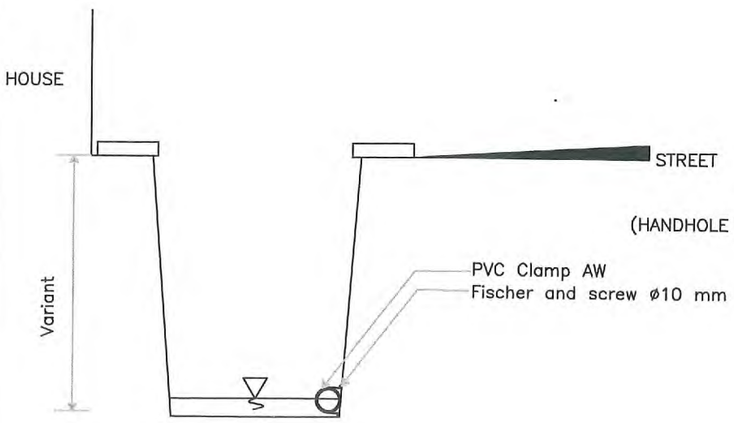

CROSS SECTION VIEW

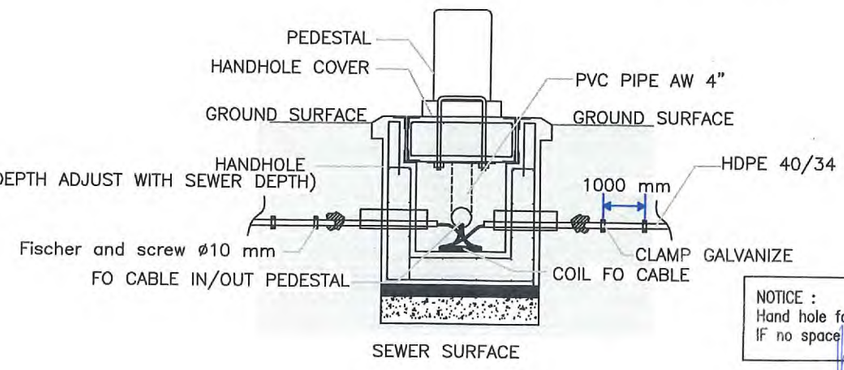

CROSS SECTION VIEW

LEGEND

HUB / CENTRAL OFFICE	HH HANDHOLE
SUB HUB / OPTICAL LINE TERMINAL	UNDERGROUND PEDESTAL
FDT FIBER DISTRIBUTION TERMINAL	EXISTING PLN POLE
FAT FIBER ACCESS TERMINAL	NP PROPOSED NEW POLE
OTB OPTICAL TERMINATION BOX	GARDU PLN
PON SPLITTER WITH x SPLIT RATIO	STO RUMAH KABEL TELKOM
ONT-RES (RESIDENTIAL) OPTICAL NETWORK TERMINAL	CR CABLE RISER
ONT-MDU (BUILDING) OPTICAL NETWORK TERMINAL	BA BORING ASPAL
FIBER OPTIC CLOSURE	GA GALI ASPAL
FIGURE EIGHT / FIBER SPARE COIL	GT GALI TANAH
MH MANHOLE	GR GALI RUMPUT

DROPWIRE 2 CORE	FIBER 12/1T
AERIAL STRAND	FIBER 24/2T
UNDERGROUND STRAND	FIBER 48/4T
UG DROP DUCT	FIBER 72/6T
FEEDER CABLE ROUTE	FIBER 96/8T
	FIBER 144/12T
	FIBER 288/24T

Keterangan
Note

No.	DATE	REVISION	SIGN

NOTICE :
Hand hole follow standard design pack.
IF no space available or no permit aquired, hand hole may not implemented

APPROVAL MATRIX		
Planning Dept.	Engineering Dept.	Project Dept.
Operation Dept.		Vendor/Contractor

PT. EKA MAS REPUBLIK
MyRepublic
Graha FIM
JL. Cik Di Tiro No.37, menteng
Jakarta Pusat 10320
Tel:+6221 3199 2626

PT. HUAWEI TECH INVESTMENT
HUAWEI
BRI II Building, 17th-22nd Floor
JL. Jend. Sudirman Kav.44-45
Jakarta Pusat 10210 – Indonesia
Tel:+6221 2555 2888 – Fax:+6221 571 3178

Nama Proyek / Project Name

Tipe Gambar / Drawing Type
TYPICAL DESIGN PACK

Sewer Installation

Digambar / Drawn — Tanggal / Date

Diperiksa / Checked — Tanggal / Date

Hub Plan Name / Nama Rencana Hub — OLT/ Sub Hub Plan Name / Nama Rencana OLT / Sub Hub

Kordinat FDT / Ref / Coordinated FDT / Ref — Revisi / Revision

Ref. Peta / Map Ref. — No. Gambar / Drawing No.

Arah / Direction — Skala / Scale: N.T.S

Halaman / Page: 15 OF 15