




PROPOSE FAT MUST IN PROPER LOCATION (MIDDLE OF TWO HOUSE OR IN STREET HOOK)

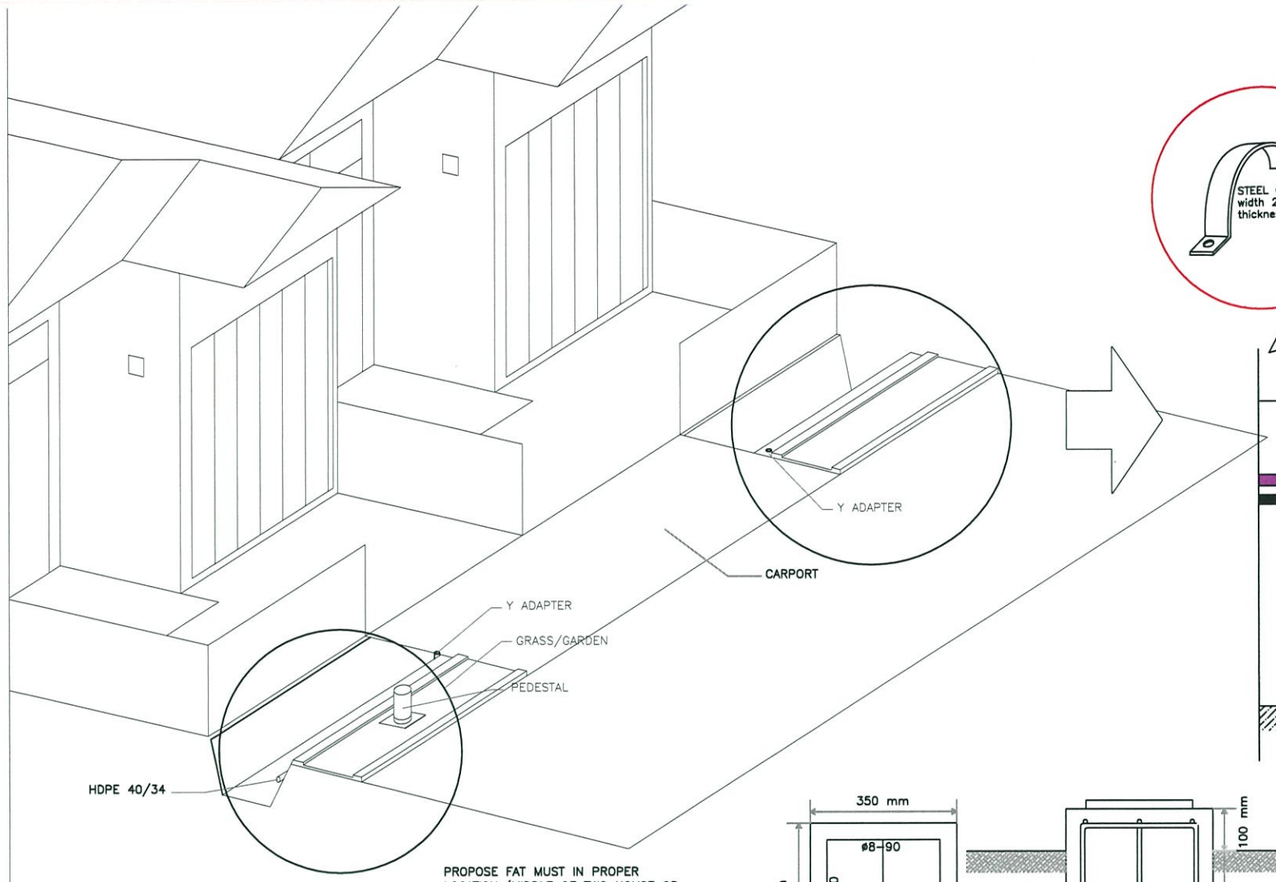


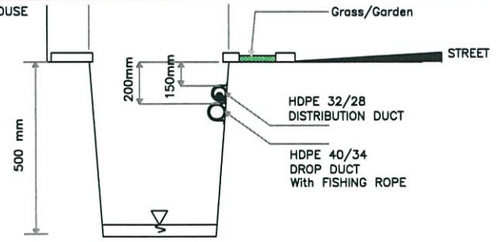

CROSS SECTION VIEW

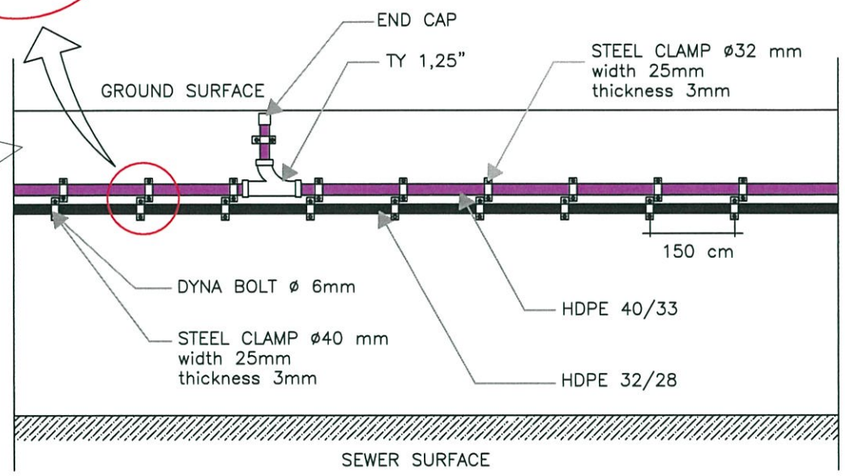


SIDE VIEW

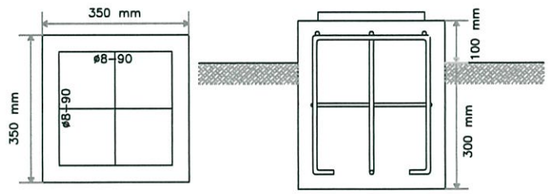


TOP VIEW SIDE VIEW

PEDESTAL BASE

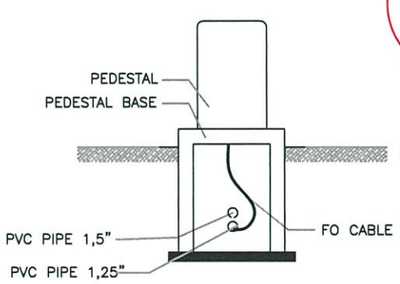


SIDE VIEW

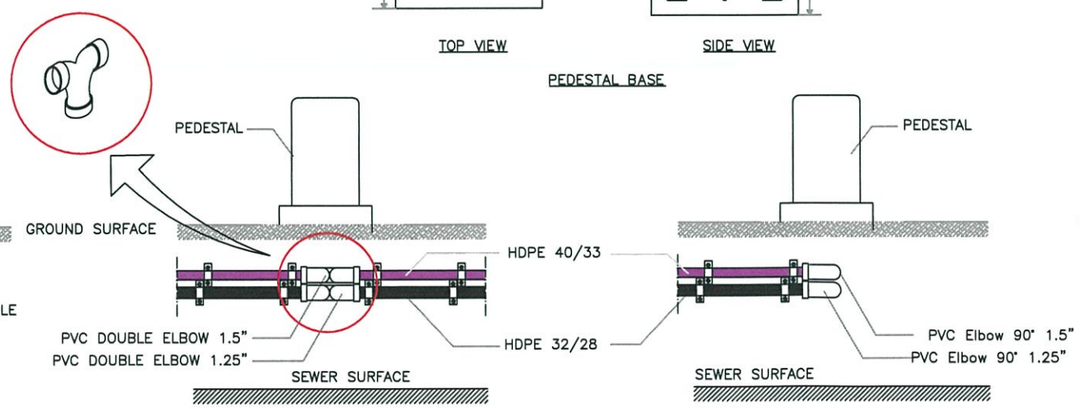

FRONT VIEW
CENTRE LINE POSITION

FRONT VIEW
END LINE POSITION

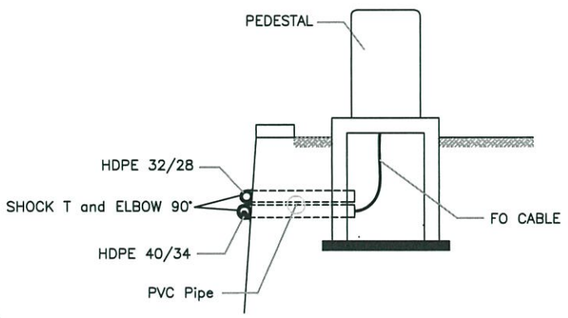

SIDE VIEW

DISCLAIMER :
1. THIS SOLUTION IS FOR CLUSTER WHICH NOT HAVE AVAILABLE SPACE FOR UNDERGROUND TOPOLOGY AND USE SEWER PART
2. THIS SEWER SOLUTION CAN BE APPLICABLE WITH CONDITION BOTH OPEN SEWER OR CLOSED SEWER WITH SEWER CAP CAN OPEN AS LONG THE SPACE IS STILL AVAILABLE
3. THIS SOLUTION IS COME FROM MYREPUBLIC AND HUAWEI ONLY PROVIDE DESIGN, IF THE COMMUNITY REFUSE THIS SOLUTION THEN THE CLUSTER WILL BE RETURN TO MYREPUBLIC

APPROVAL MATRIX		
Planning Dept.	Engineering Dept.	Project Dept.
Operation Dept.		Vendor/Contractor

CENTRAL OFFICE	HANDHOLE
SUB HUB / OPTICAL LINE TERMINAL	UNDERGROUND PEDESTAL
FDT FIBER DISTRIBUTION TERMINAL	EXISTING PLN POLE
FAT FIBER ACCESS TERMINAL	NP PROPOSED NEW POLE
OTB OPTICAL TERMINATION BOX	GARDU PLN
PON SPLITTER WITH x SPLIT RATIO	STO RUMAH KABEL TELKOM
ONT–RES (RESIDENTIAL) OPTICAL NETWORK TERMINAL	CR CABLE RISER
ONT–MDU (BUILDING) OPTICAL NETWORK TERMINAL	BA BORING ASPAL
FIBER OPTIC CLOSURE	GA GALI ASPAL
FIGURE EIGHT / FIBER SPARE COIL	GT GALI TANAH
MH MANHOLE	GR GALI RUMPUT

DROPWIRE 2 CORE	FIBER 12/1T
AERIAL STRAND	FIBER 24/2T
UNDERGROUND STRAND	FIBER 48/4T
UG DROP DUCT	FIBER 72/6T
FEEDER CABLE ROUTE	FIBER 96/8T
	FIBER 144/12T
	FIBER 288/24T

Keterangan
Note

No.	DATE	REVISION	SIGN

My Republic
My Republic Plaza 1st floor
BSD Green Office Park 6, Jalan Grand Boulevard
Tangerang Selatan 15345

PT. HUAWEI TECH INVESTMENT
BRI II Building, 17th–22nd Floor
JL. Jend. Sudirman Kav.44–46
Jakarta Pusat 10210 – Indonesia
Tel: +6221 2555 2888 – Fax: +6221 571 3178

Nama Proyek / Project Name

Tipe Gambar / Drawing Type
TYPICAL DESIGN PACK

Sewer Installation without handhole

Digambar / Drawn — Tanggal / Date

Diperiksa / Checked — Tanggal / Date

Hub Plan Name / Nama Rencana Hub — OLT/ Sub Hub Plan Name / Nama Rencana OLT / Sub Hub

Koordinat FDT / Ref / Coordinated FDT / Ref — Revisi / Revision

Ref. Peta / Map Ref. — No. Gambar / Drawing No.

Arah / Direction — Skala / Scale: N.T.S

Halaman / Page: 01 OF 01