


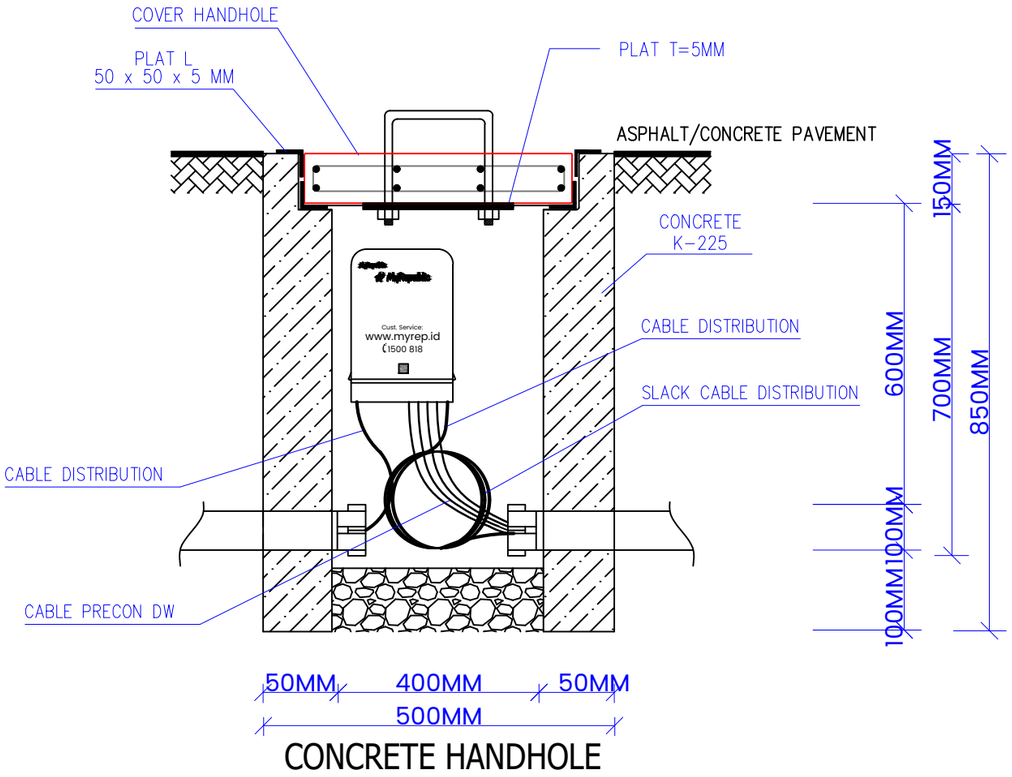



CONCRETE HANDHOLE

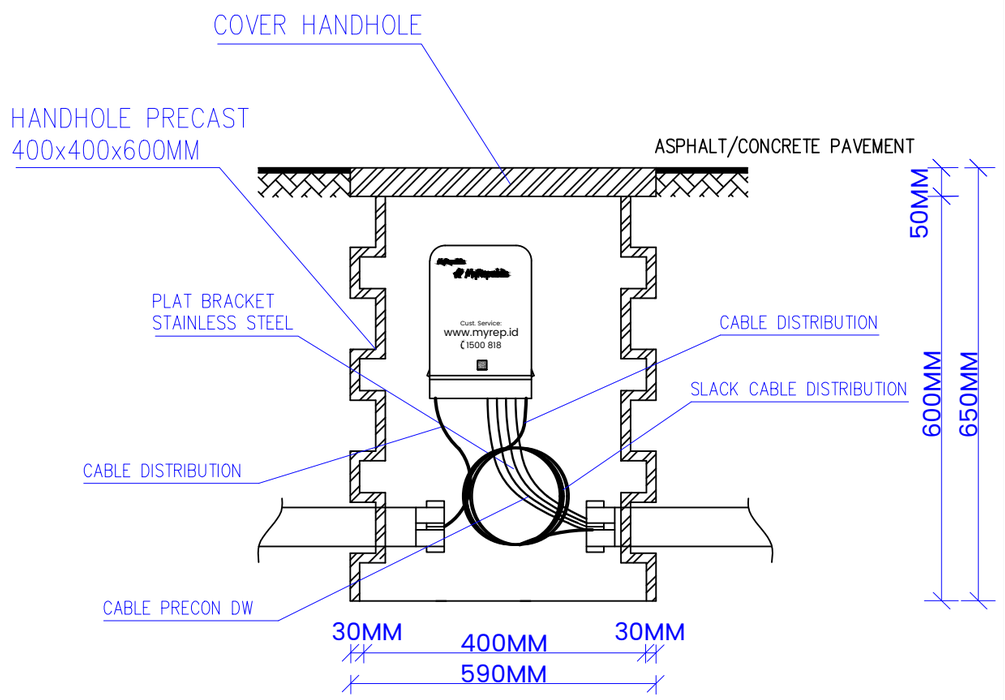

PRECAST HANDHOLE

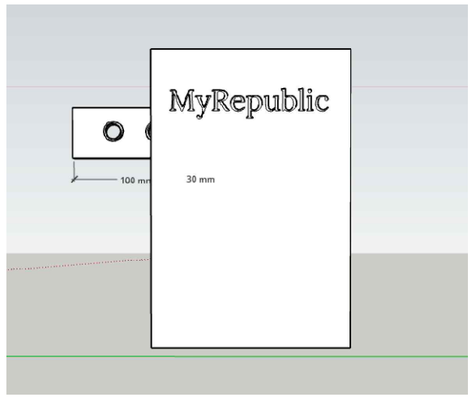

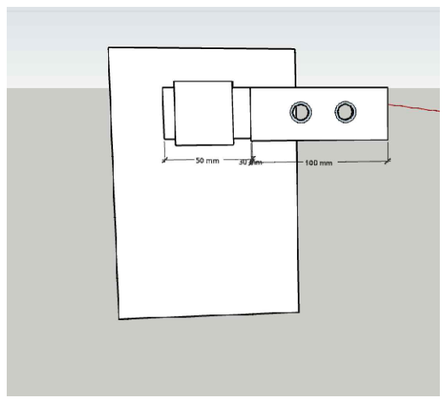

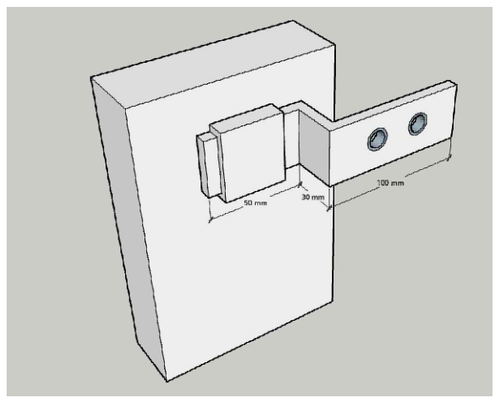

BRACKET SOLUTION

TABLE INFORMATION	
MATERIAL	PLAT ANTI KARAT (STAINLESS STEEL)
BRACKET DIMENSION	150 X 40 X 3 MM

LEGEND

HUB / CENTRAL OFFICE	HANDHOLE 40X40X60
SUB HUB / OPTICAL LINE TERMINAL	UNDERGROUND PEDESTAL
FIBER DISTRIBUTION TERMINAL	PROPOSES NEW POLE 9m
FIBER ACCESS TERMINAL / FAT **= SPLITTER CONFIG	PROPOSED NEW POLE 7m
OPTICAL TERMINATION BOX	GARDU PLN
HANDHOLE 80X80X130	RUMAH KABEL TELKOM
HANDHOLE 20X20X20	LABEL CABLE
ONT-RES (RESIDENTIAL) OPTICAL NETWORK TERMINAL	LARGE TEE RADIUS
ONT-MDU (BUILDING) OPTICAL NETWORK TERMINAL	CABLE RISER
FIBER OPTIC CLOSURE	BORING ASPAL / BORING ASPHALT WORK
FIGURE EIGHT / FIBER SPARE COIL	BORING TANAH / BORING SOIL WORK
Sidewalk Guy Down Guy	GALI TANAH / TRENCHING TYPE WORK

CABLE TYPE

AERIAL STRAND	FIBER 12/2T
UNDERGROUND STRAND	FIBER 24/4T
UG DROP DUCT	FIBER 36/6T
FEEDER CABLE ROUTE	FIBER 72/6T
FAT AREA LINE	FIBER 96/8T
	FIBER 144/12T
	FIBER 288/24T

APPROVAL MATRIX

PLANNING DEPT	PROJECT DEPT	OPERATION DEPT	CTO MYREPUBLIC
KRESNO AGUNG NUGROHO	PUJI YUWONO	ANGGA WISHNU WIJAYA	HENDRA GUNAWAN

MyRepublic
MYREPUBLIC PLAZA 1ST FLOOR
GREEN OFFICE PARK 6
BSD – TANGERANG 15345
Tel: +6221 319 2626

NAMA PROYEK
PROJECT NAME

STANDARD DESIGN FAT UNDERGROUND IMPLEMENTATION AT HANDHOLE 400x400x600 MM

DRAWING SIGN & CHECK

DIGAMBAR / DRAWN: WAHYU SETIYONO	TANGGAL / DATE: 03/07/2024	TANDA TANGAN / SIGNATURE
DIPERIKSA / CHECKED: SAIPULLAH HAILANI	TANGGAL / DATE: 03/07/2024	TANDA TANGAN / SIGNATURE

RIWAYAT DOKUMEN
DOCUMENT HISTORY

1. RELEASE DESIGN – 03 JULY 2024

REF. PETA / MAP REF.: –	REVISI / REVISION: –
SATUAN / UNIT: SATUAN DALAM MM	SKALA / SCALE: 1 : 400
ARAH / DIRECTION: N	NO. DOKUMEN / DOCUMENT NO: 061/UG/EMR-PLG/VII/2024
	NO. GAMBAR / DRAWING NO: 061